





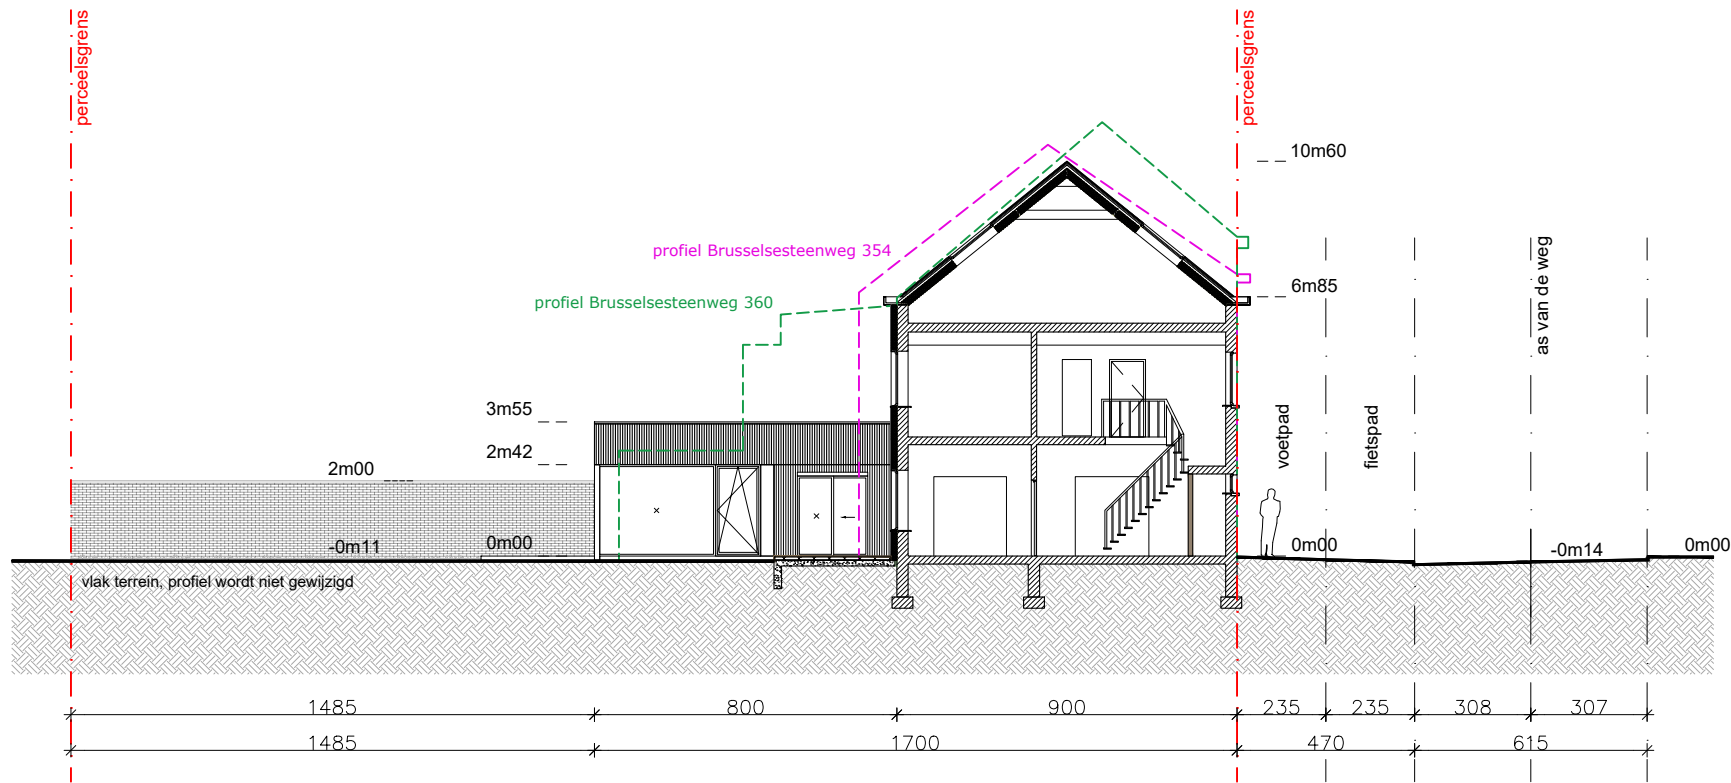

2023/07 – Noten–Wouters


verbouwen van een ééngezinwoning – Terreinprofiel – nieuwe toestand

1/200

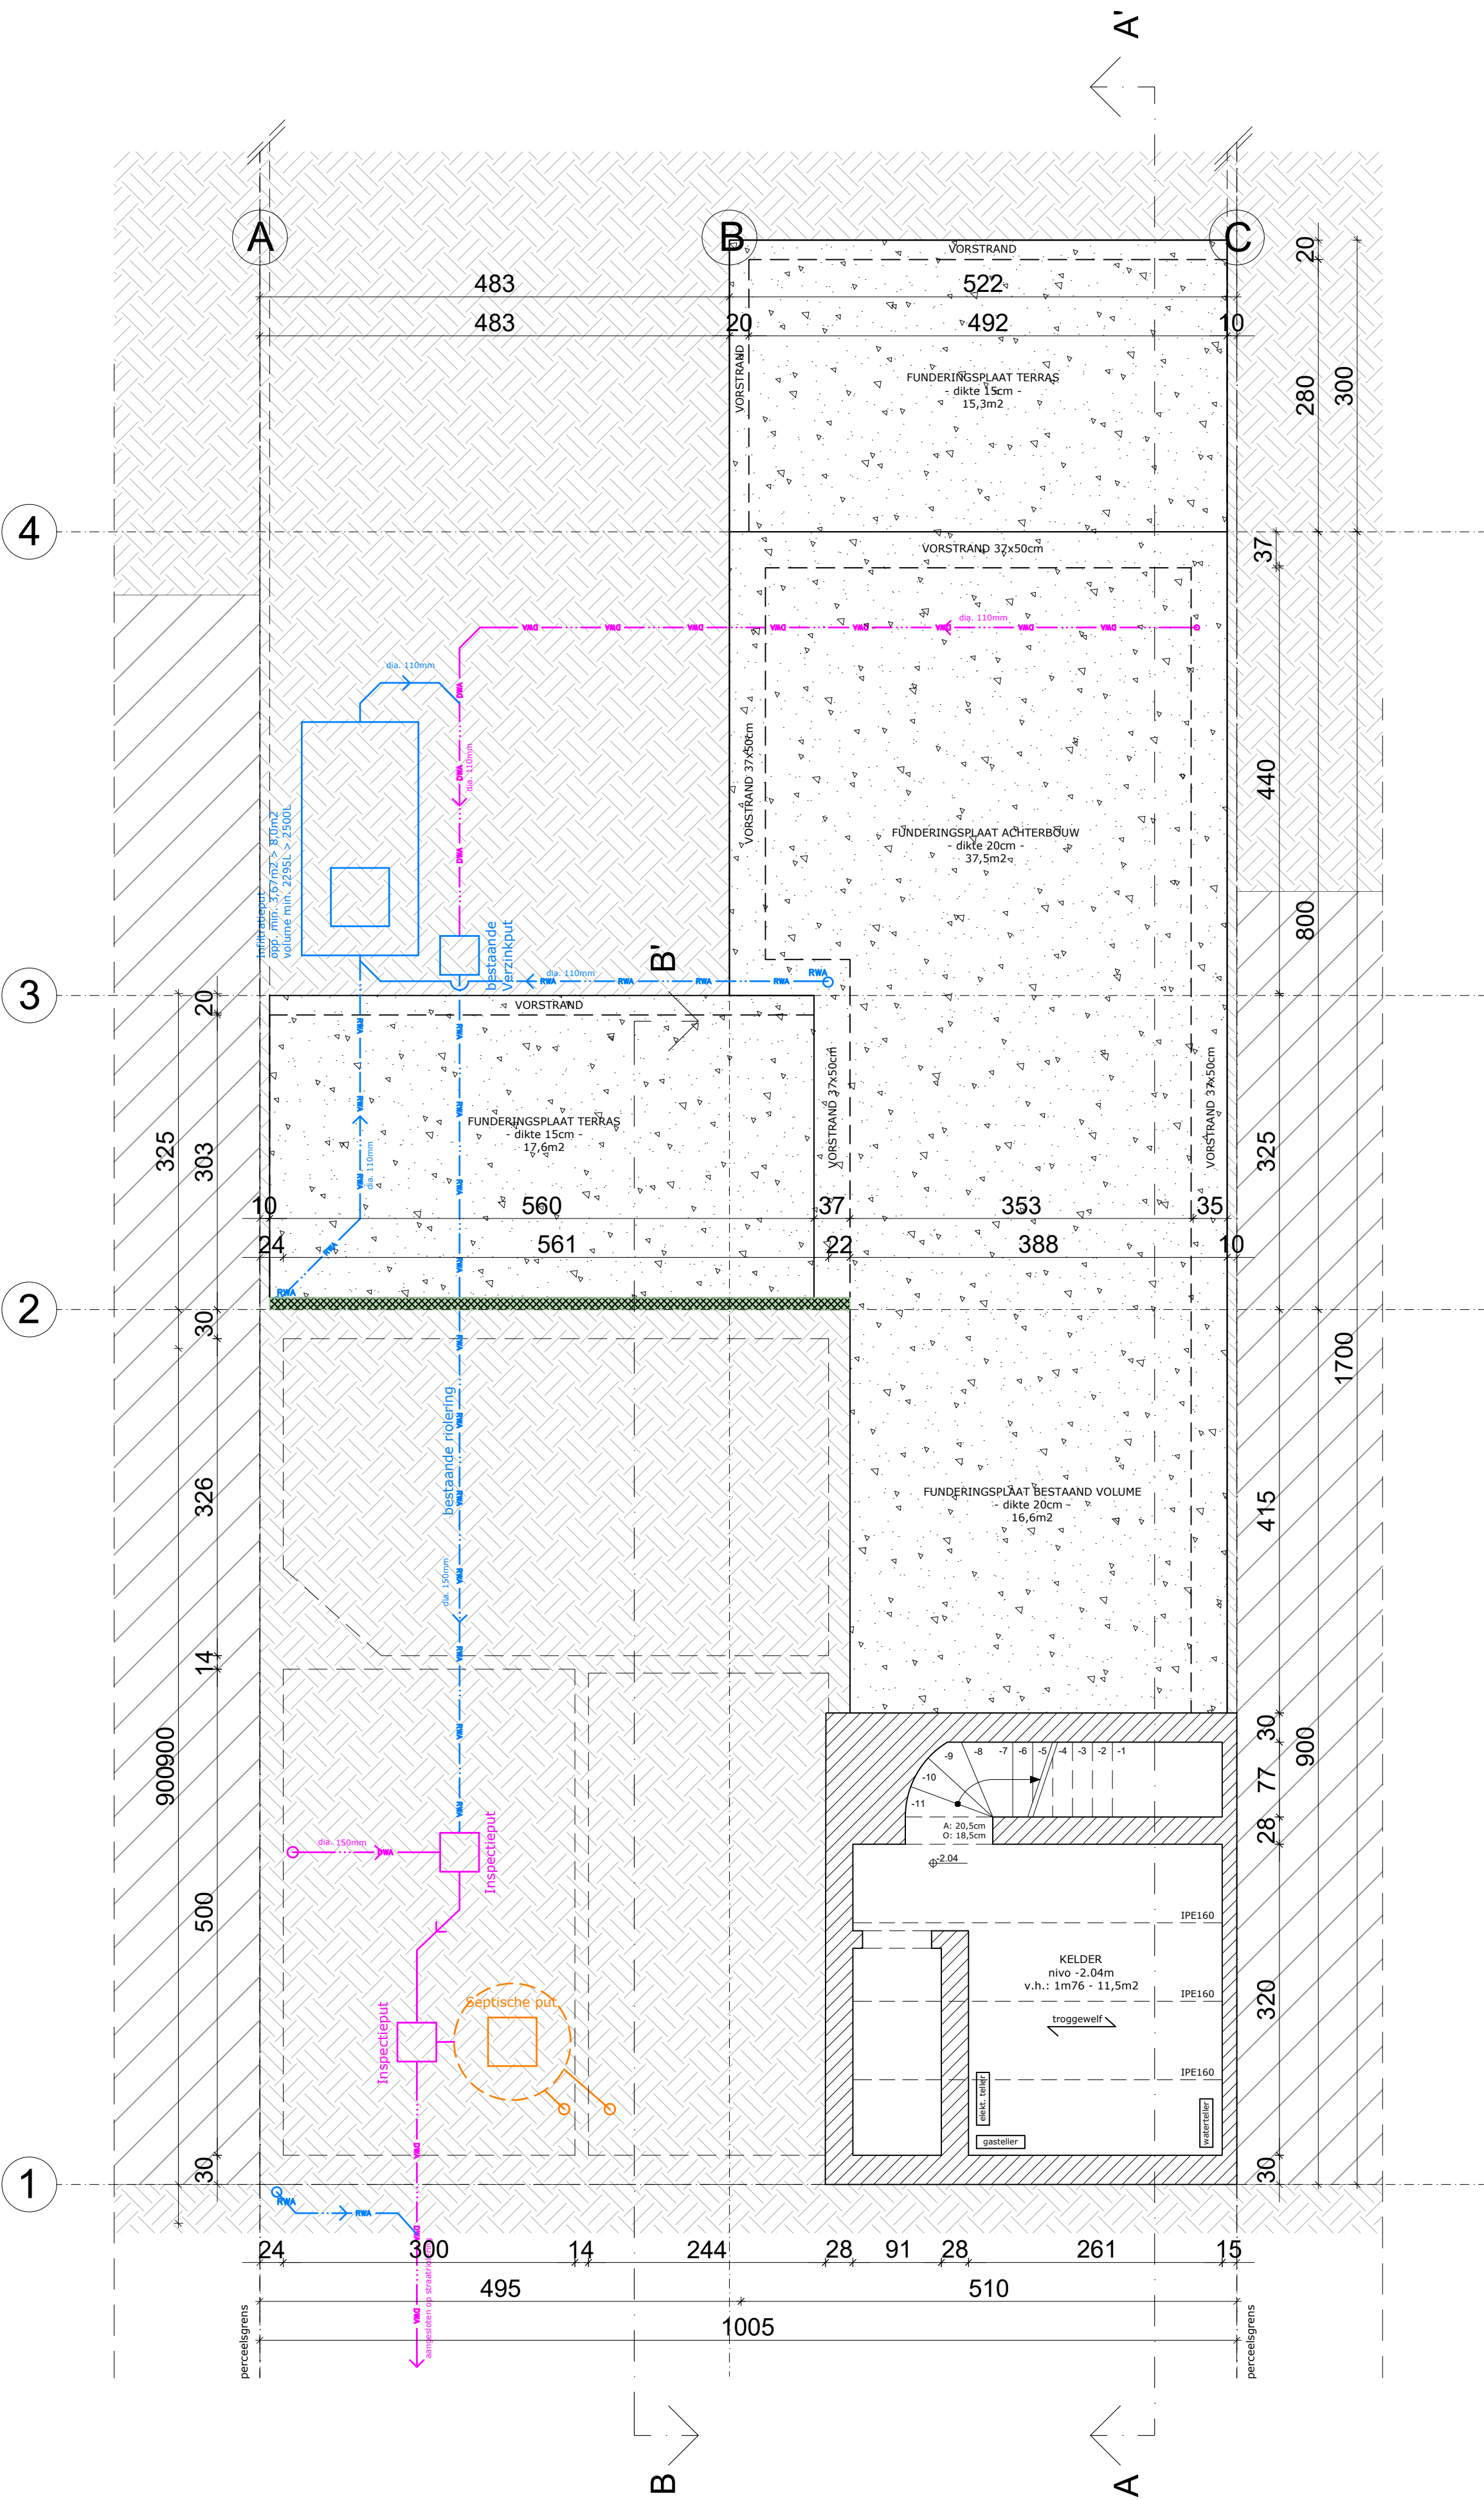







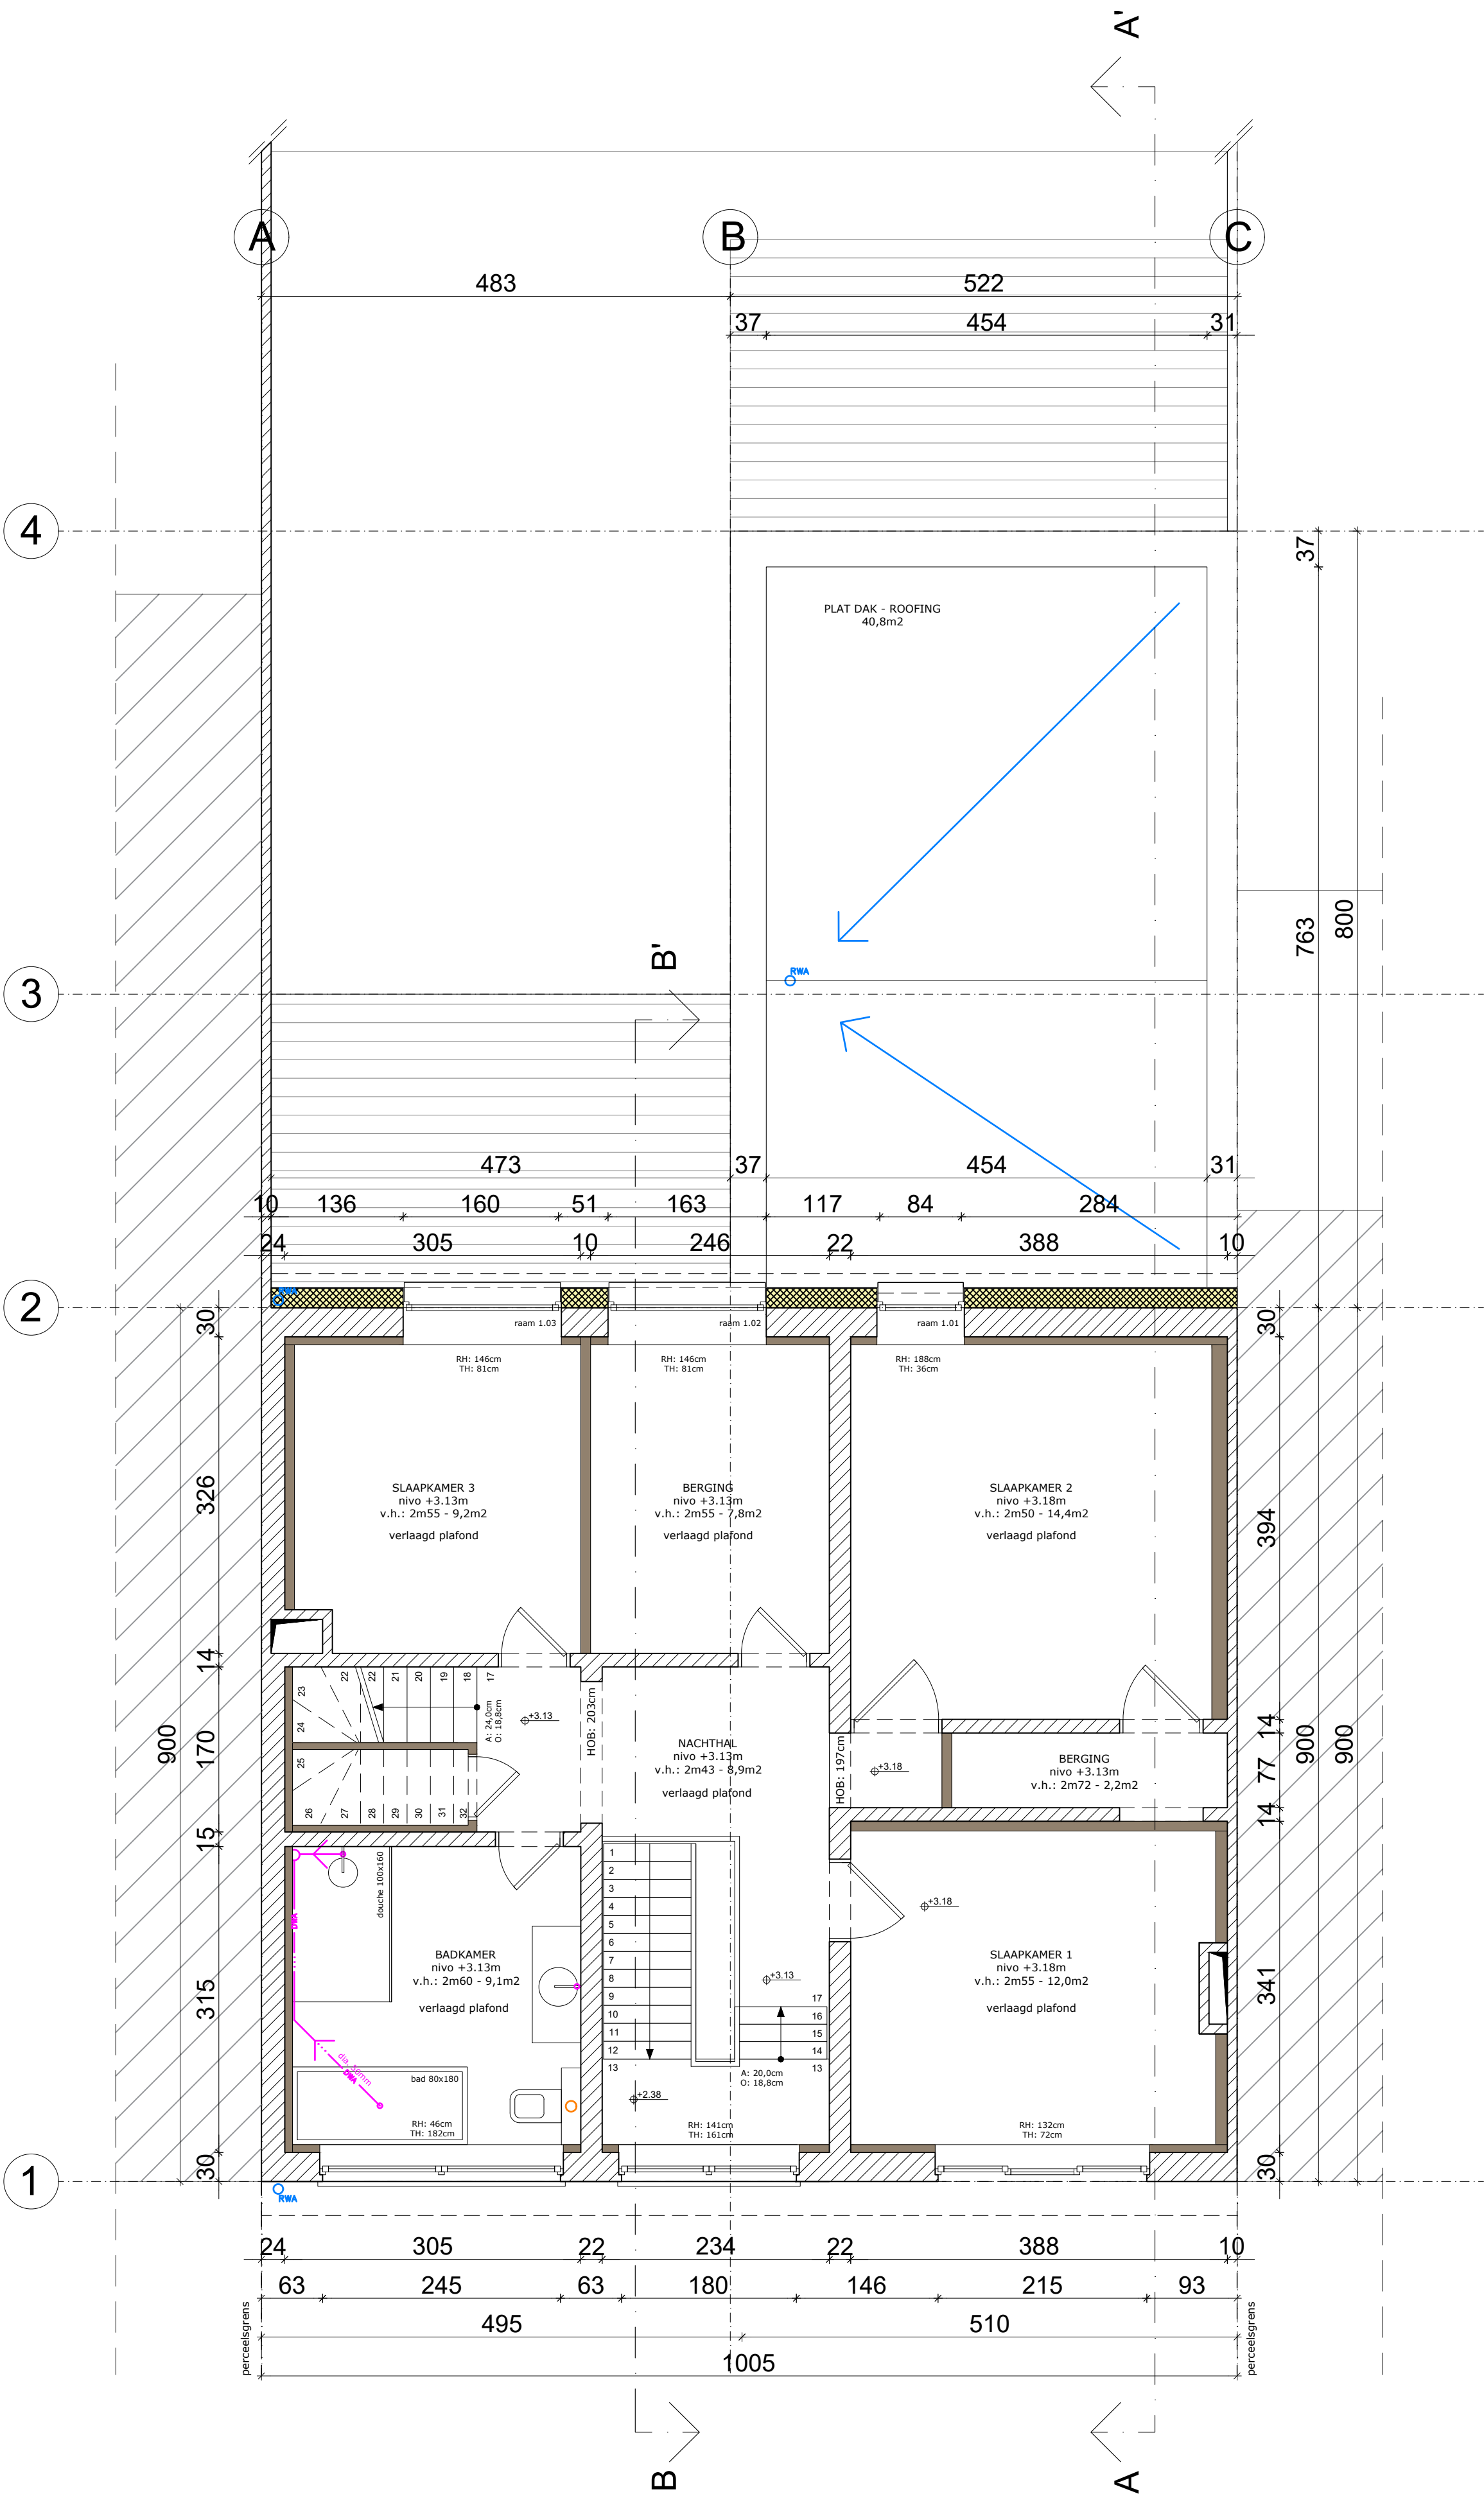




 

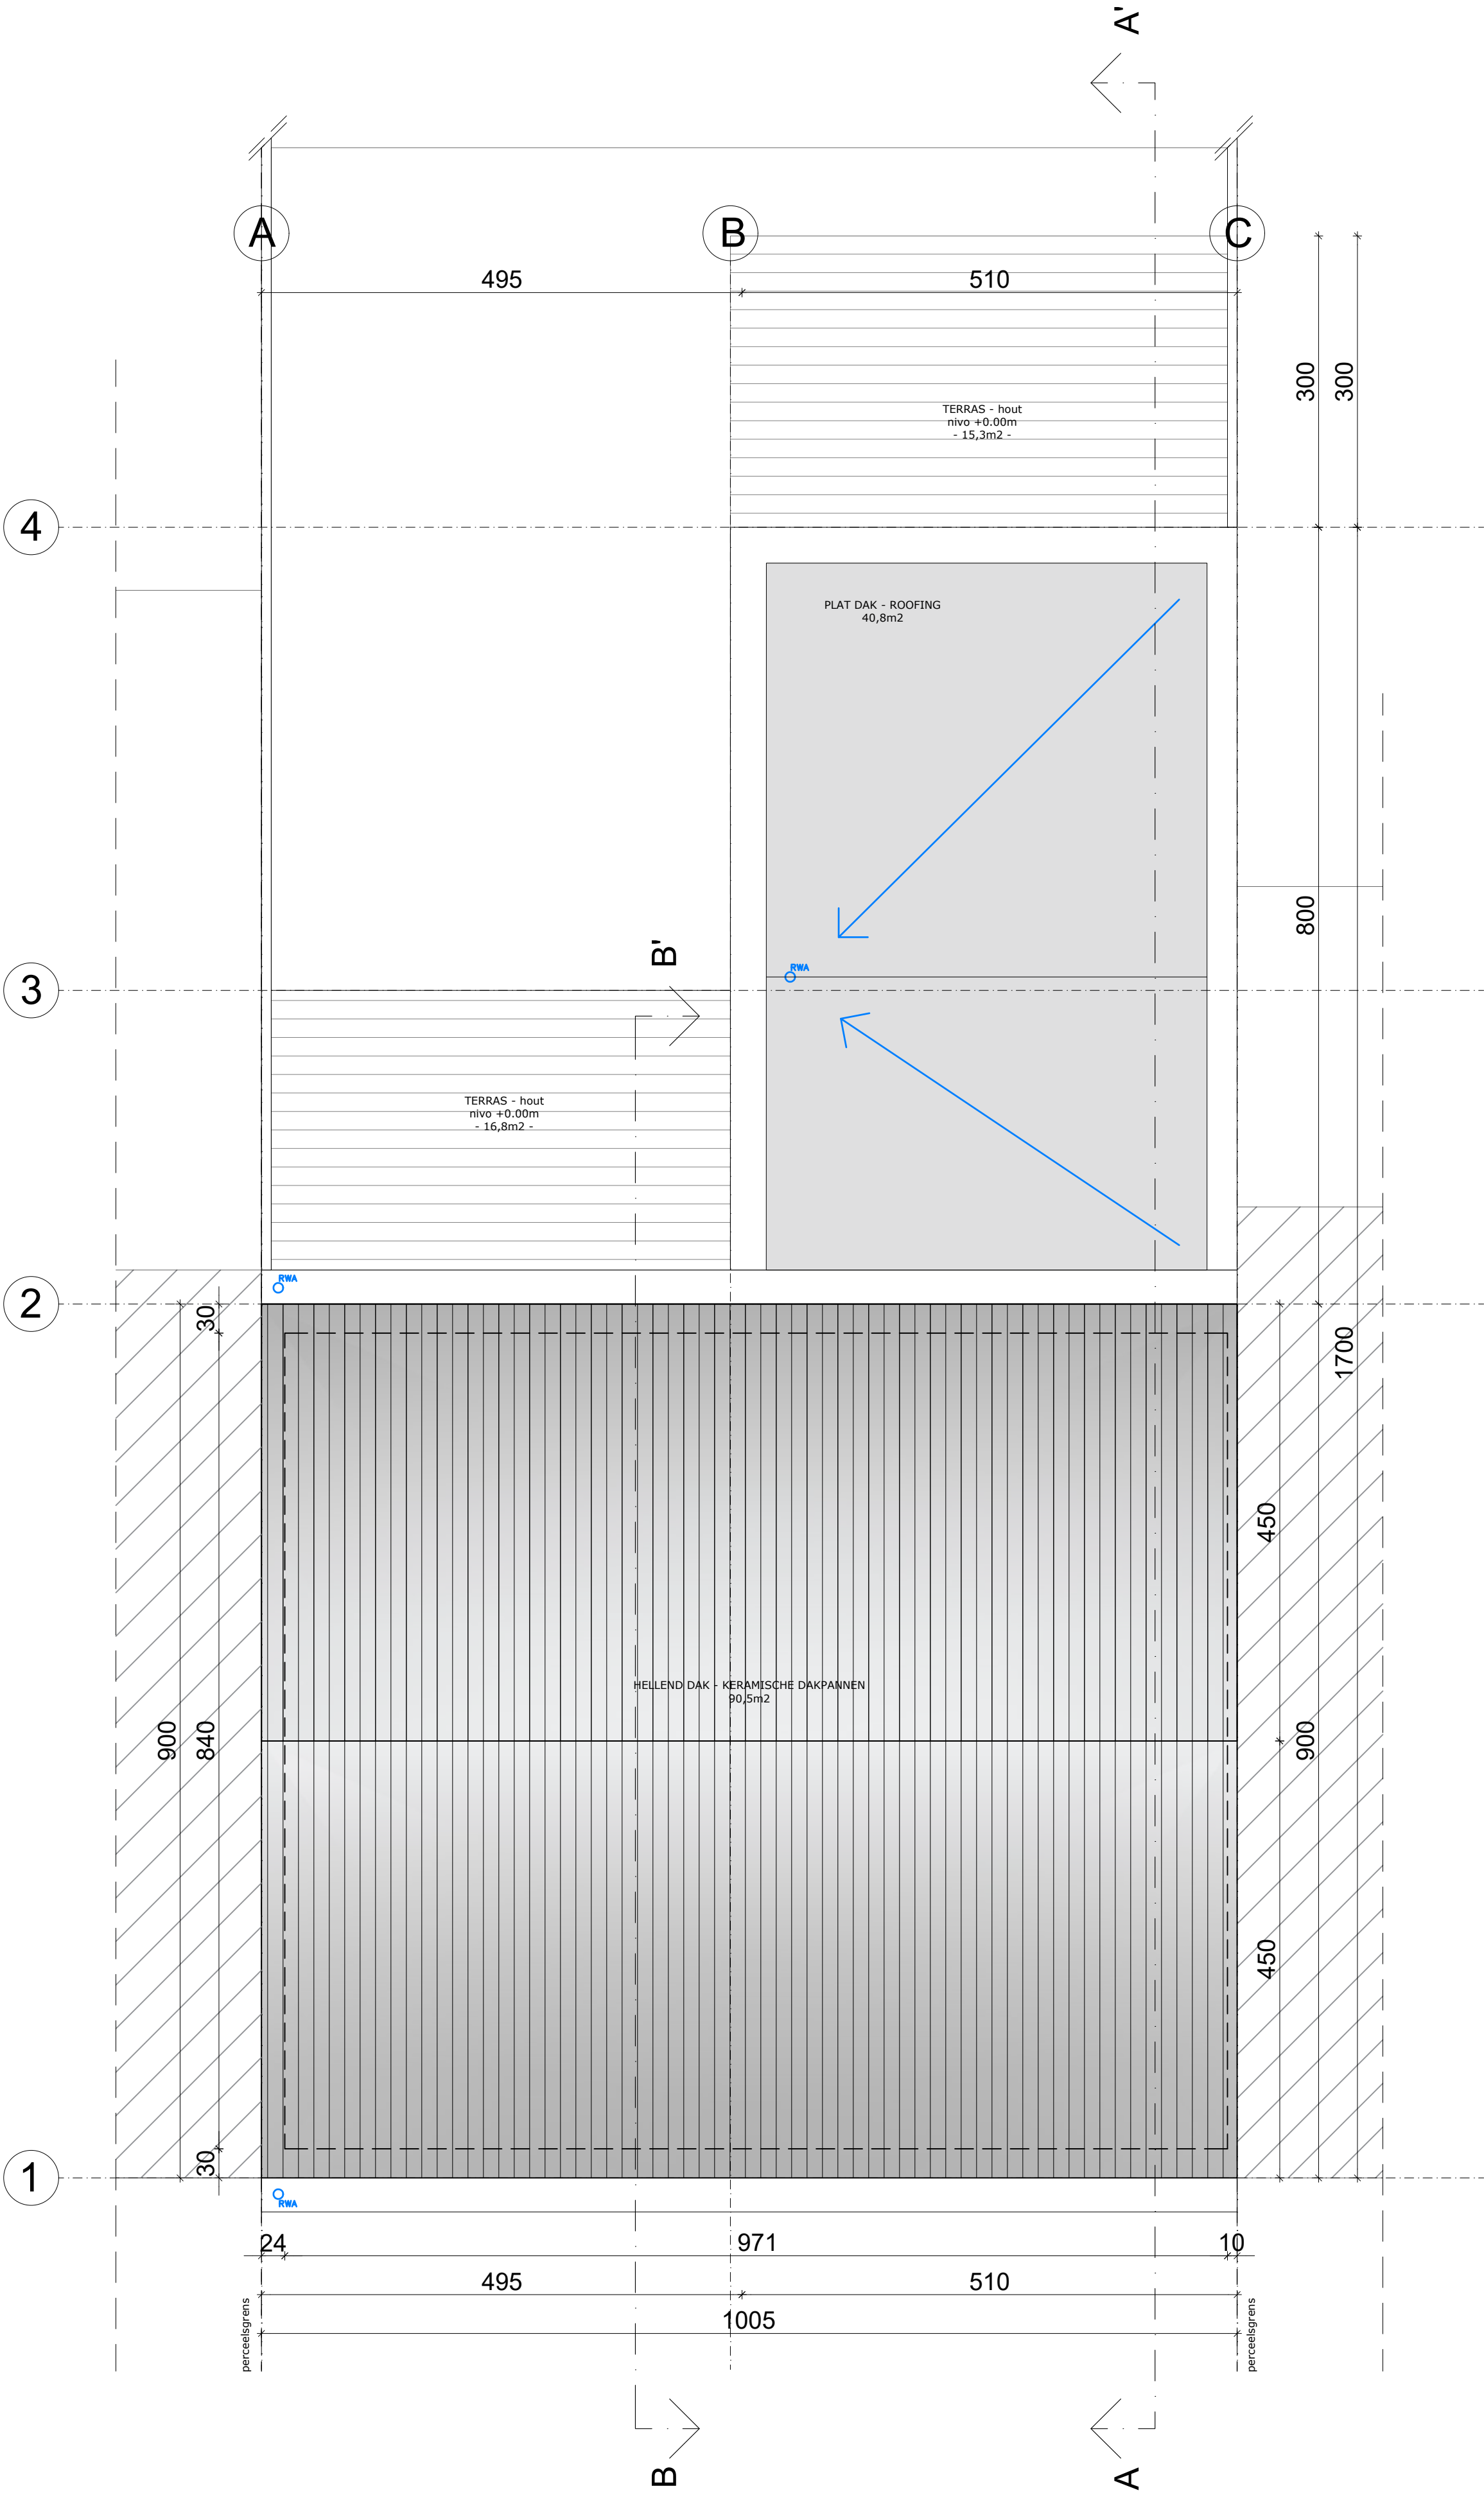






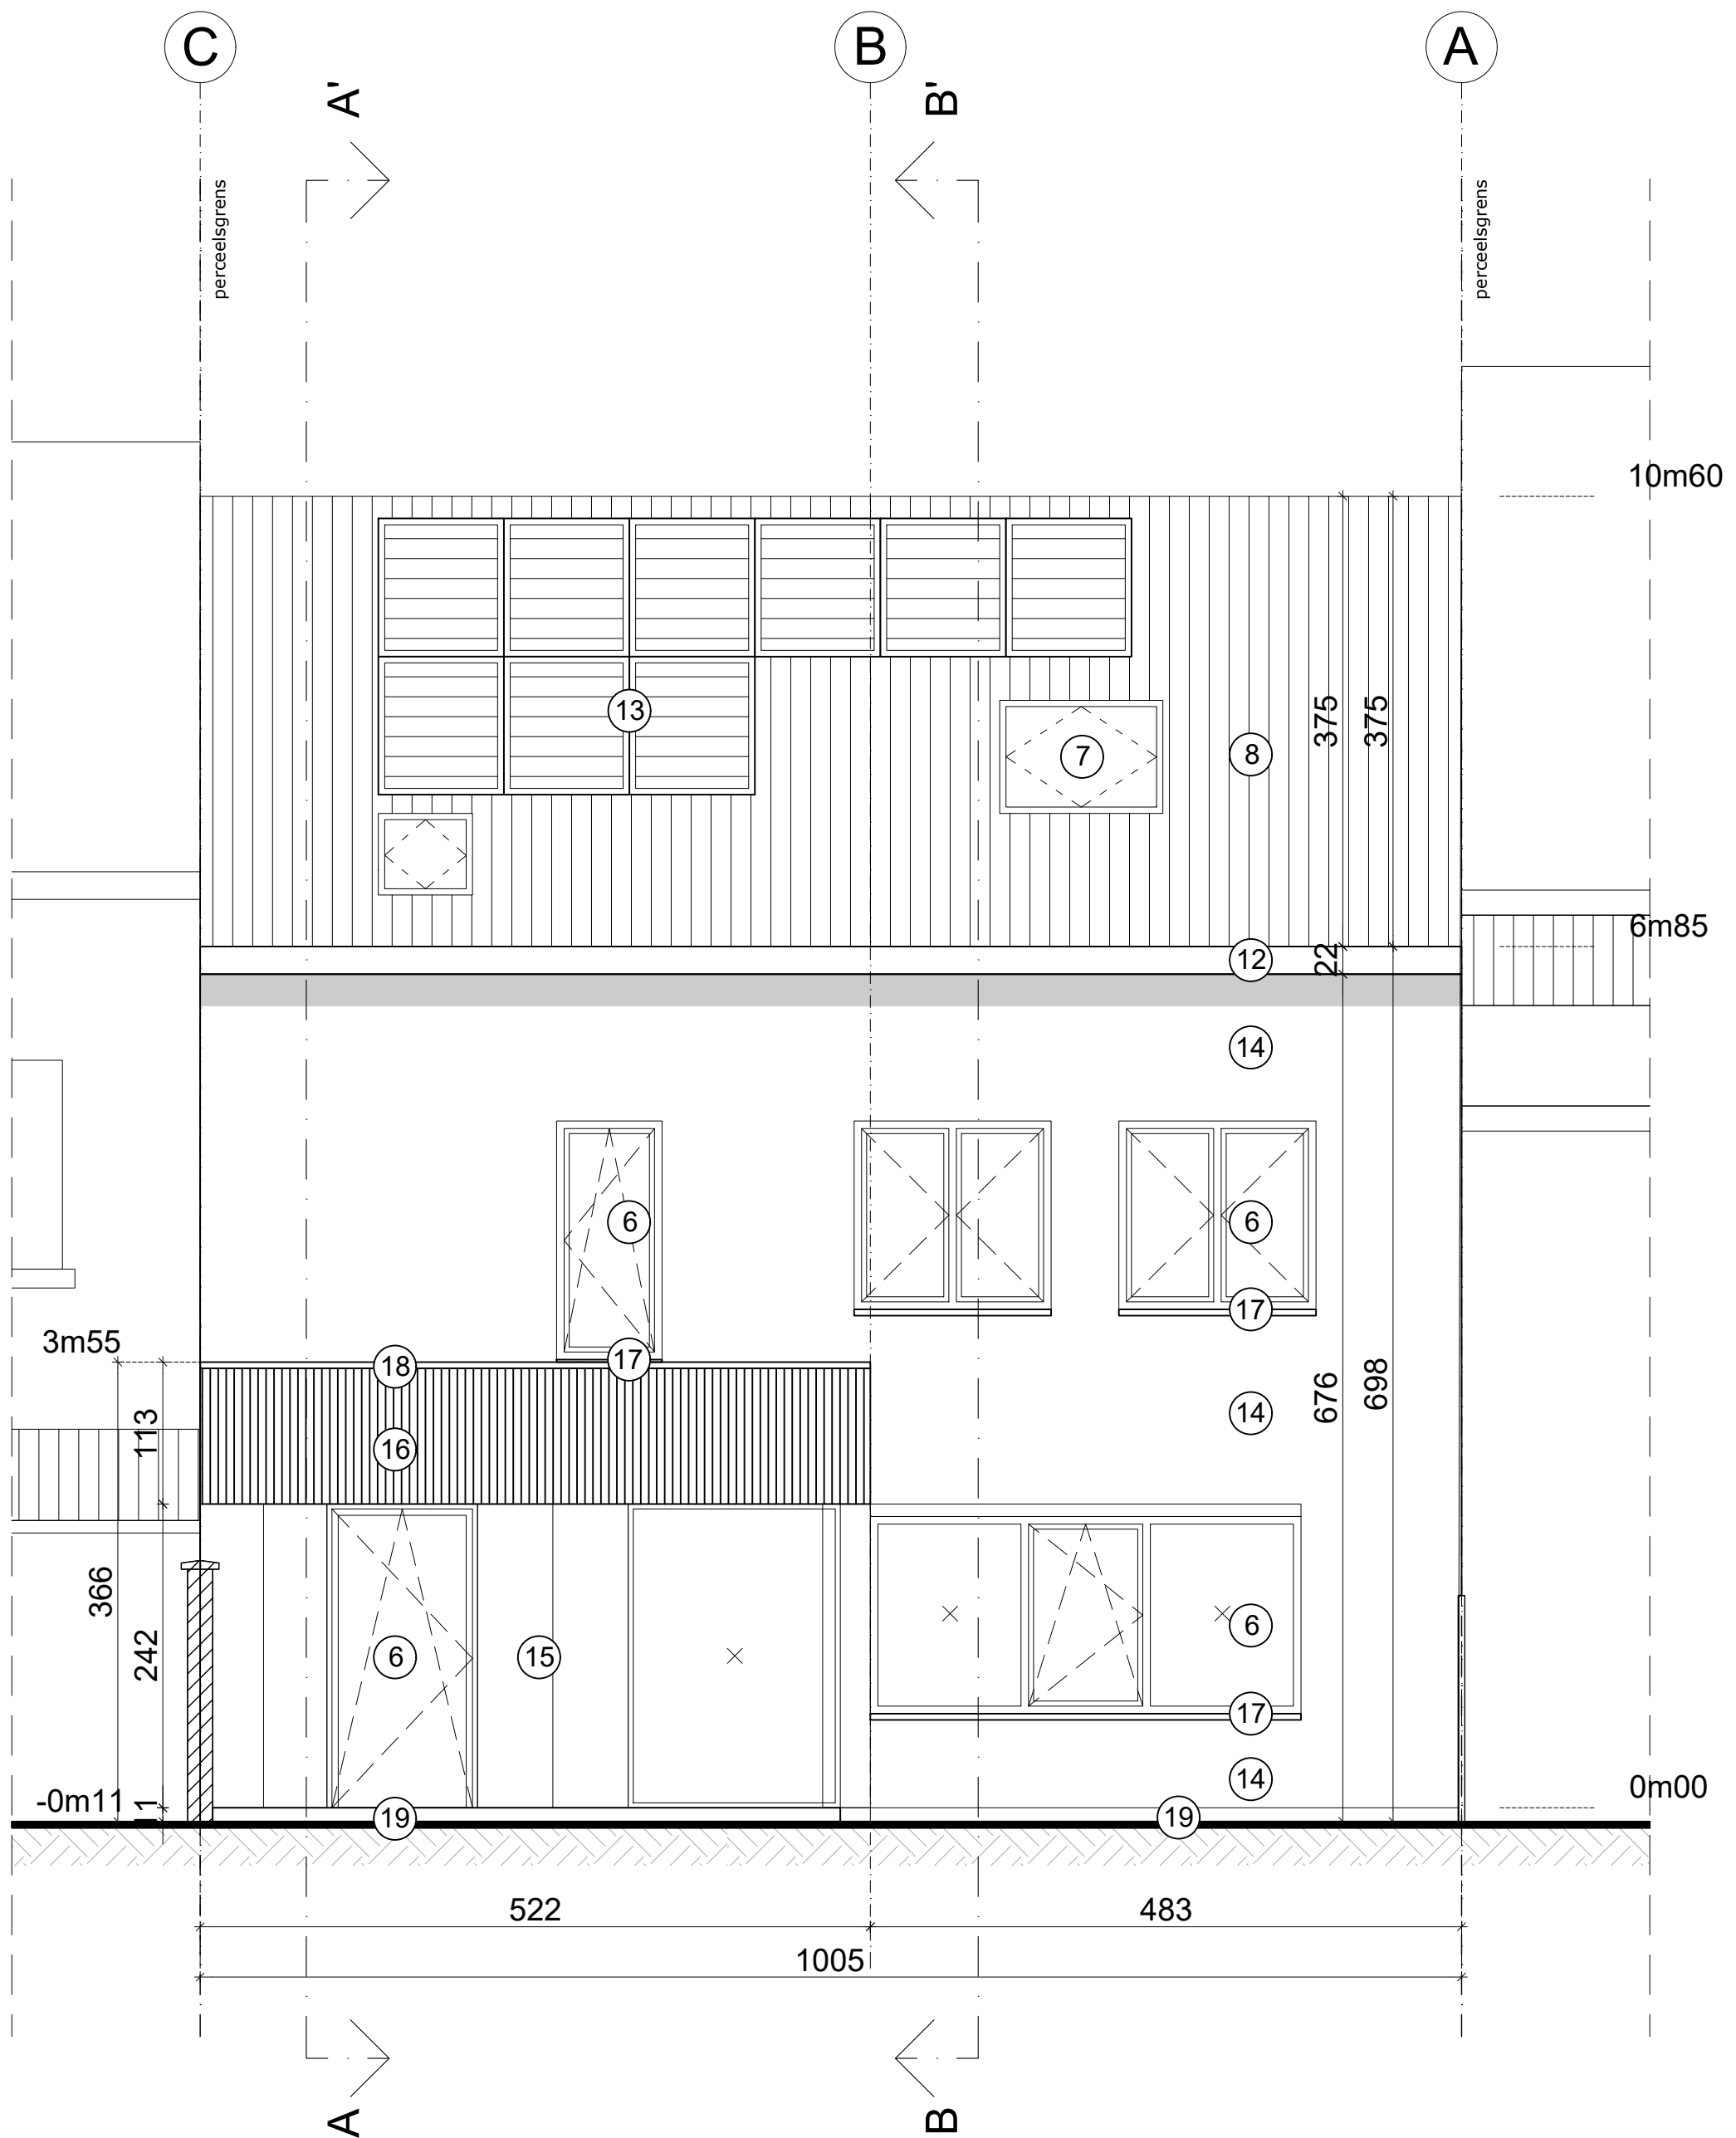



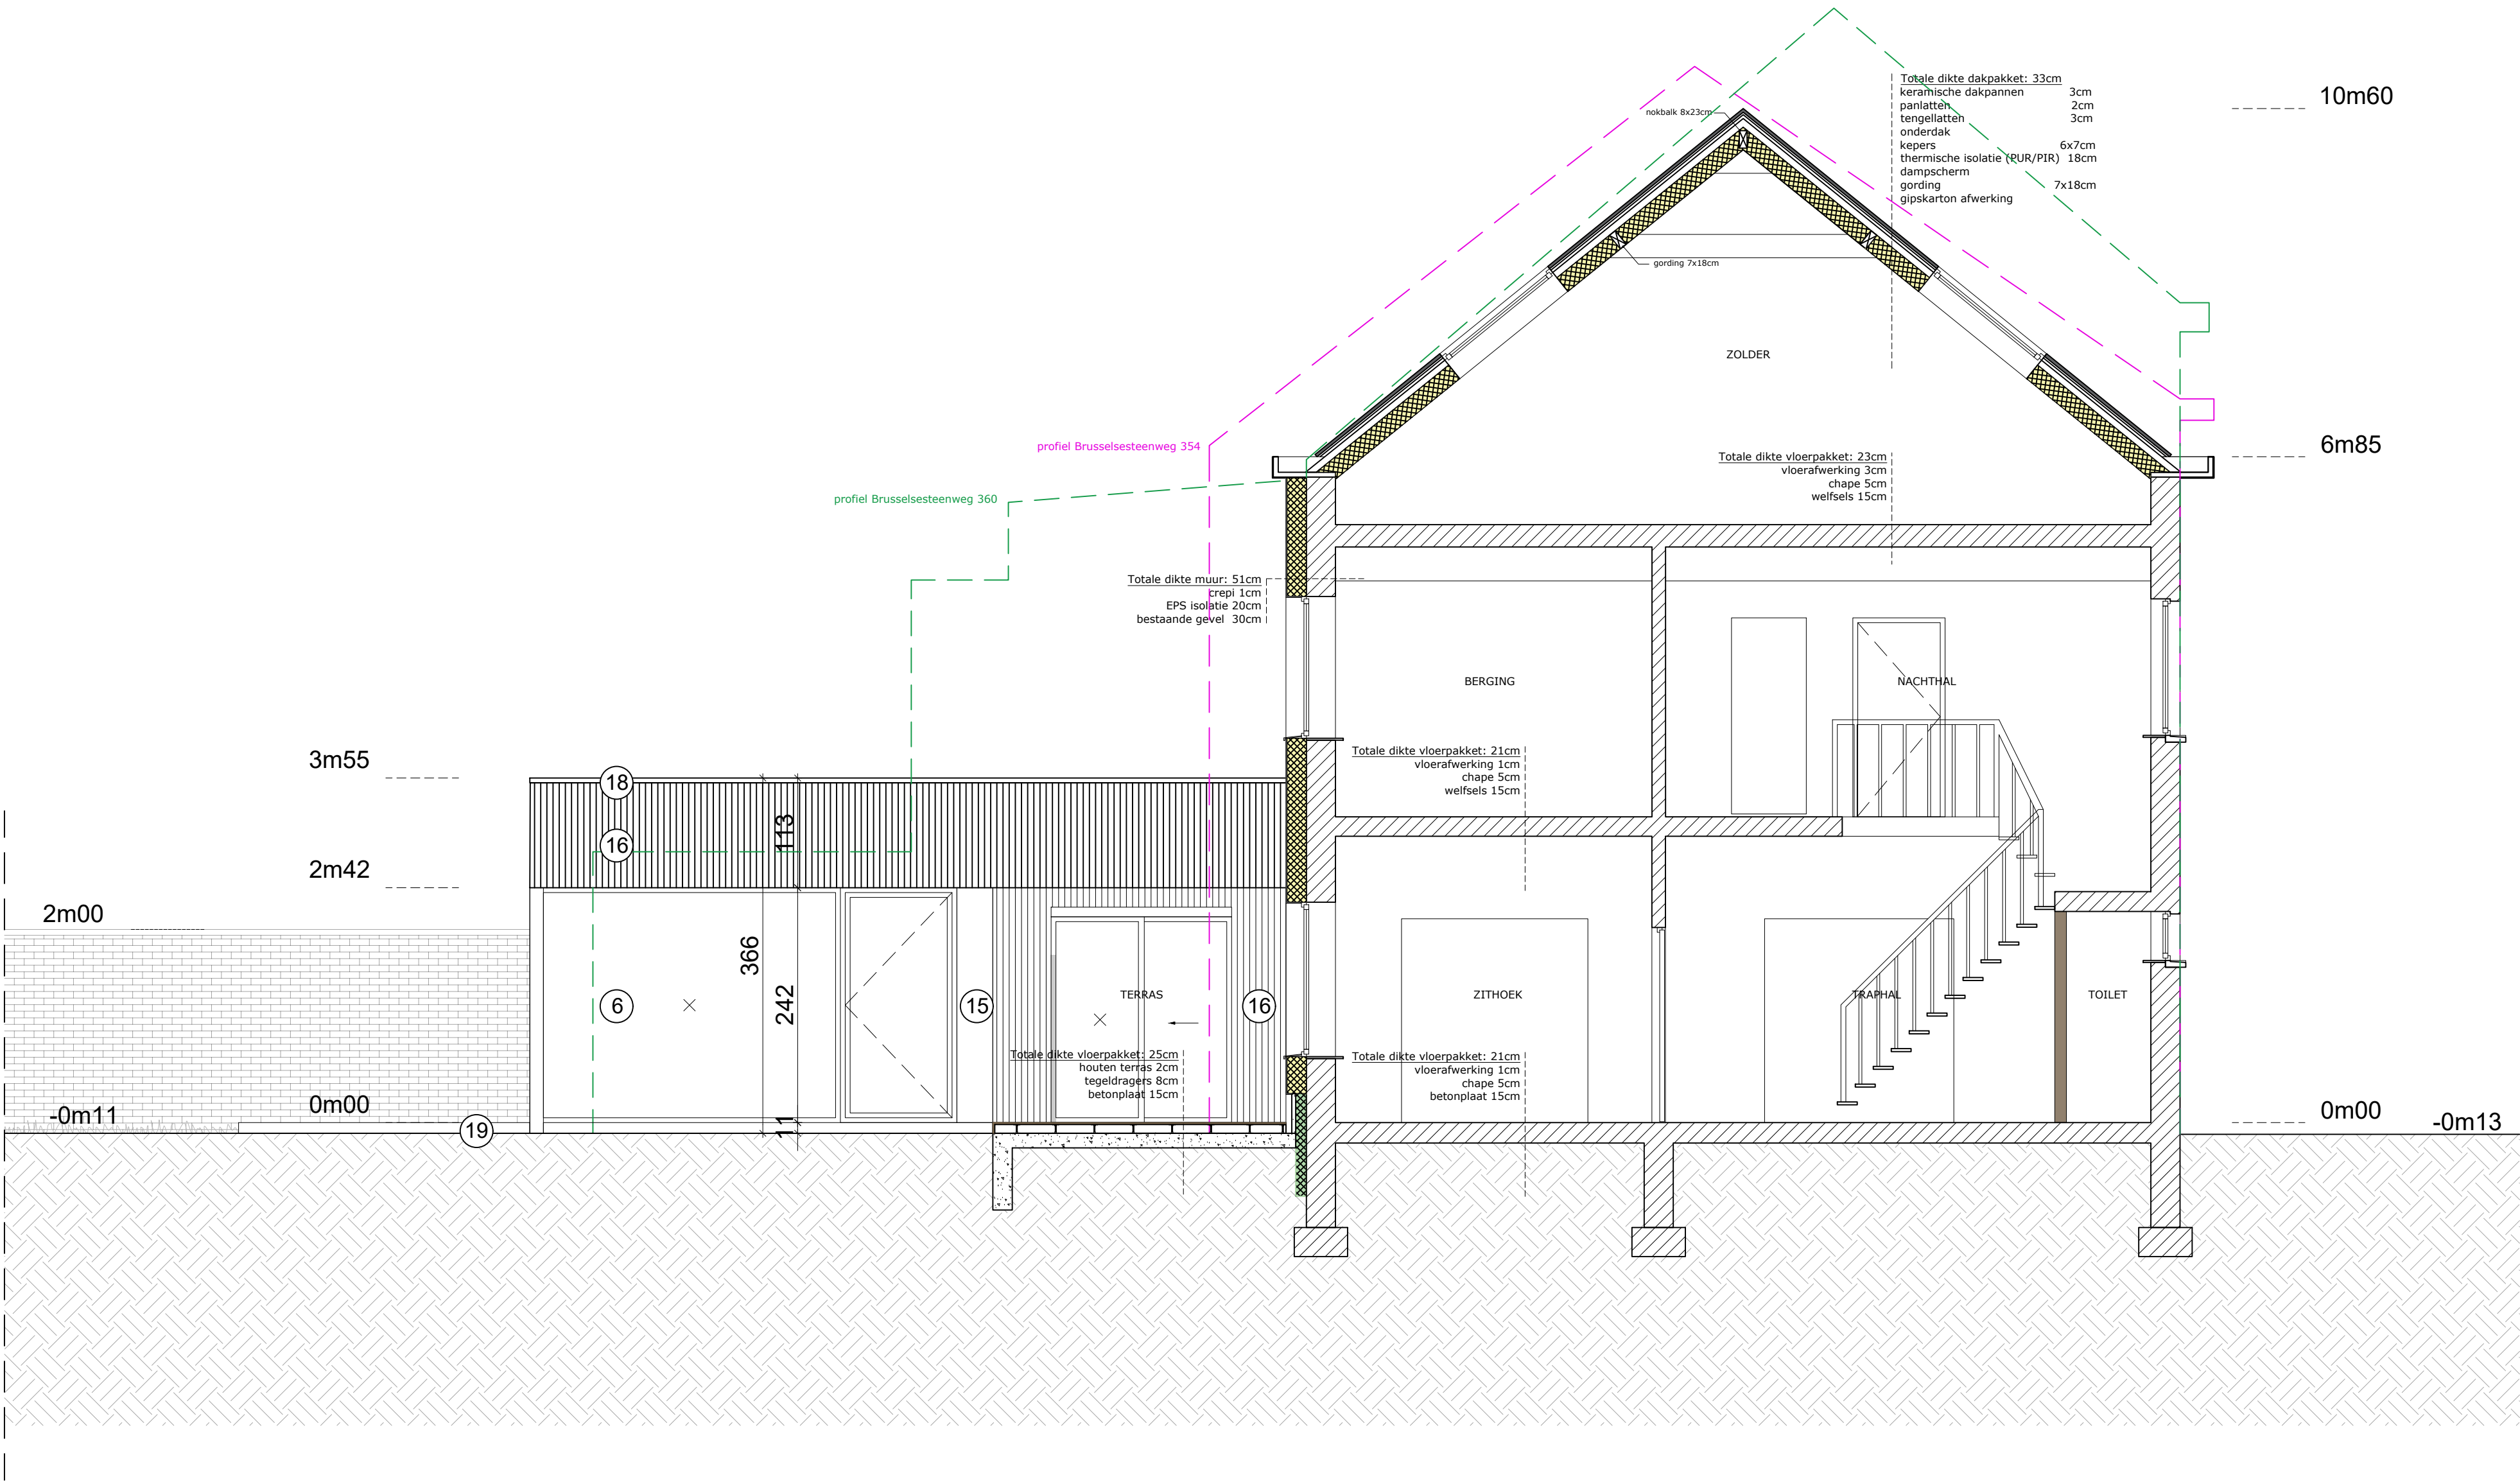

Legende grondplannen & snedes:

-  bestaande constructie
-  nieuw metselwerk
-  lichte scheidings- / voozetwand
-  beton
-  chape
-  isolerend metselwerk - ytong
-  thermische isolatie (PUR/PIR/EPS)
-  thermische isolatie (XPS)
-  gevelmetselwerk - kruisverband
-  dakbedekking
-  schaduw
-  aarde
-  DWA vuilwaterafvoer (DWA) na verbouwing
-  RWA regenwaterafvoer (RWA) na verbouwing
-  FAEC bestaande fecaal waterafvoer
-  +0.00 hoogtepas afgewerkt niveau

Legende inplantingsplan:

-  perceelsgrens
-  grind
-  terras
-  struiken
-  gras

Legende gevels:

-  Gevelmetselwerk - halfsteensverband - lichtgrijze gevelsteen
-  Gevelafwerking - natuursteen - lichtgrijs
-  Gevelafwerking - gevelcementering - lichtgrijs
-  Gevelement - dorpel - blauwe hardsteen
-  Buitenschrijnwerk - ramen - aluminium - lichtgrijs
-  Buitenschrijnwerk - ramen - aluminium - kwartsgrijs (RAL 7039)
-  Buitenschrijnwerk - ramen - dakvlakraam
-  Dakbedekking - keramische dakpannen - zwart
-  Dakbedekking - kanaalplaten - transparant
-  Regenwater - regenwaterafvoer - PVC - lichtgrijs
-  Regenwater - regenwaterafvoer - PVC - antraciet
-  Kroonlijst - bakgoot - pvc bekleding - antraciet
-  Zonnepaneel
-  Gevelafwerking - EPS isolatie + crepi - wit
-  Buitenschrijnwerk - HPL plaatmateriaal - kwartsgrijs (RAL 7039)
-  Buitenschrijnwerk - hout - gevelbekleding
-  Buitenschrijnwerk - raamdorpel - aluminium - kwartsgrijs (RAL 7039)
-  Kroonlijst - aluminium dakrand - antraciet
-  Terrasafwerking - hout