




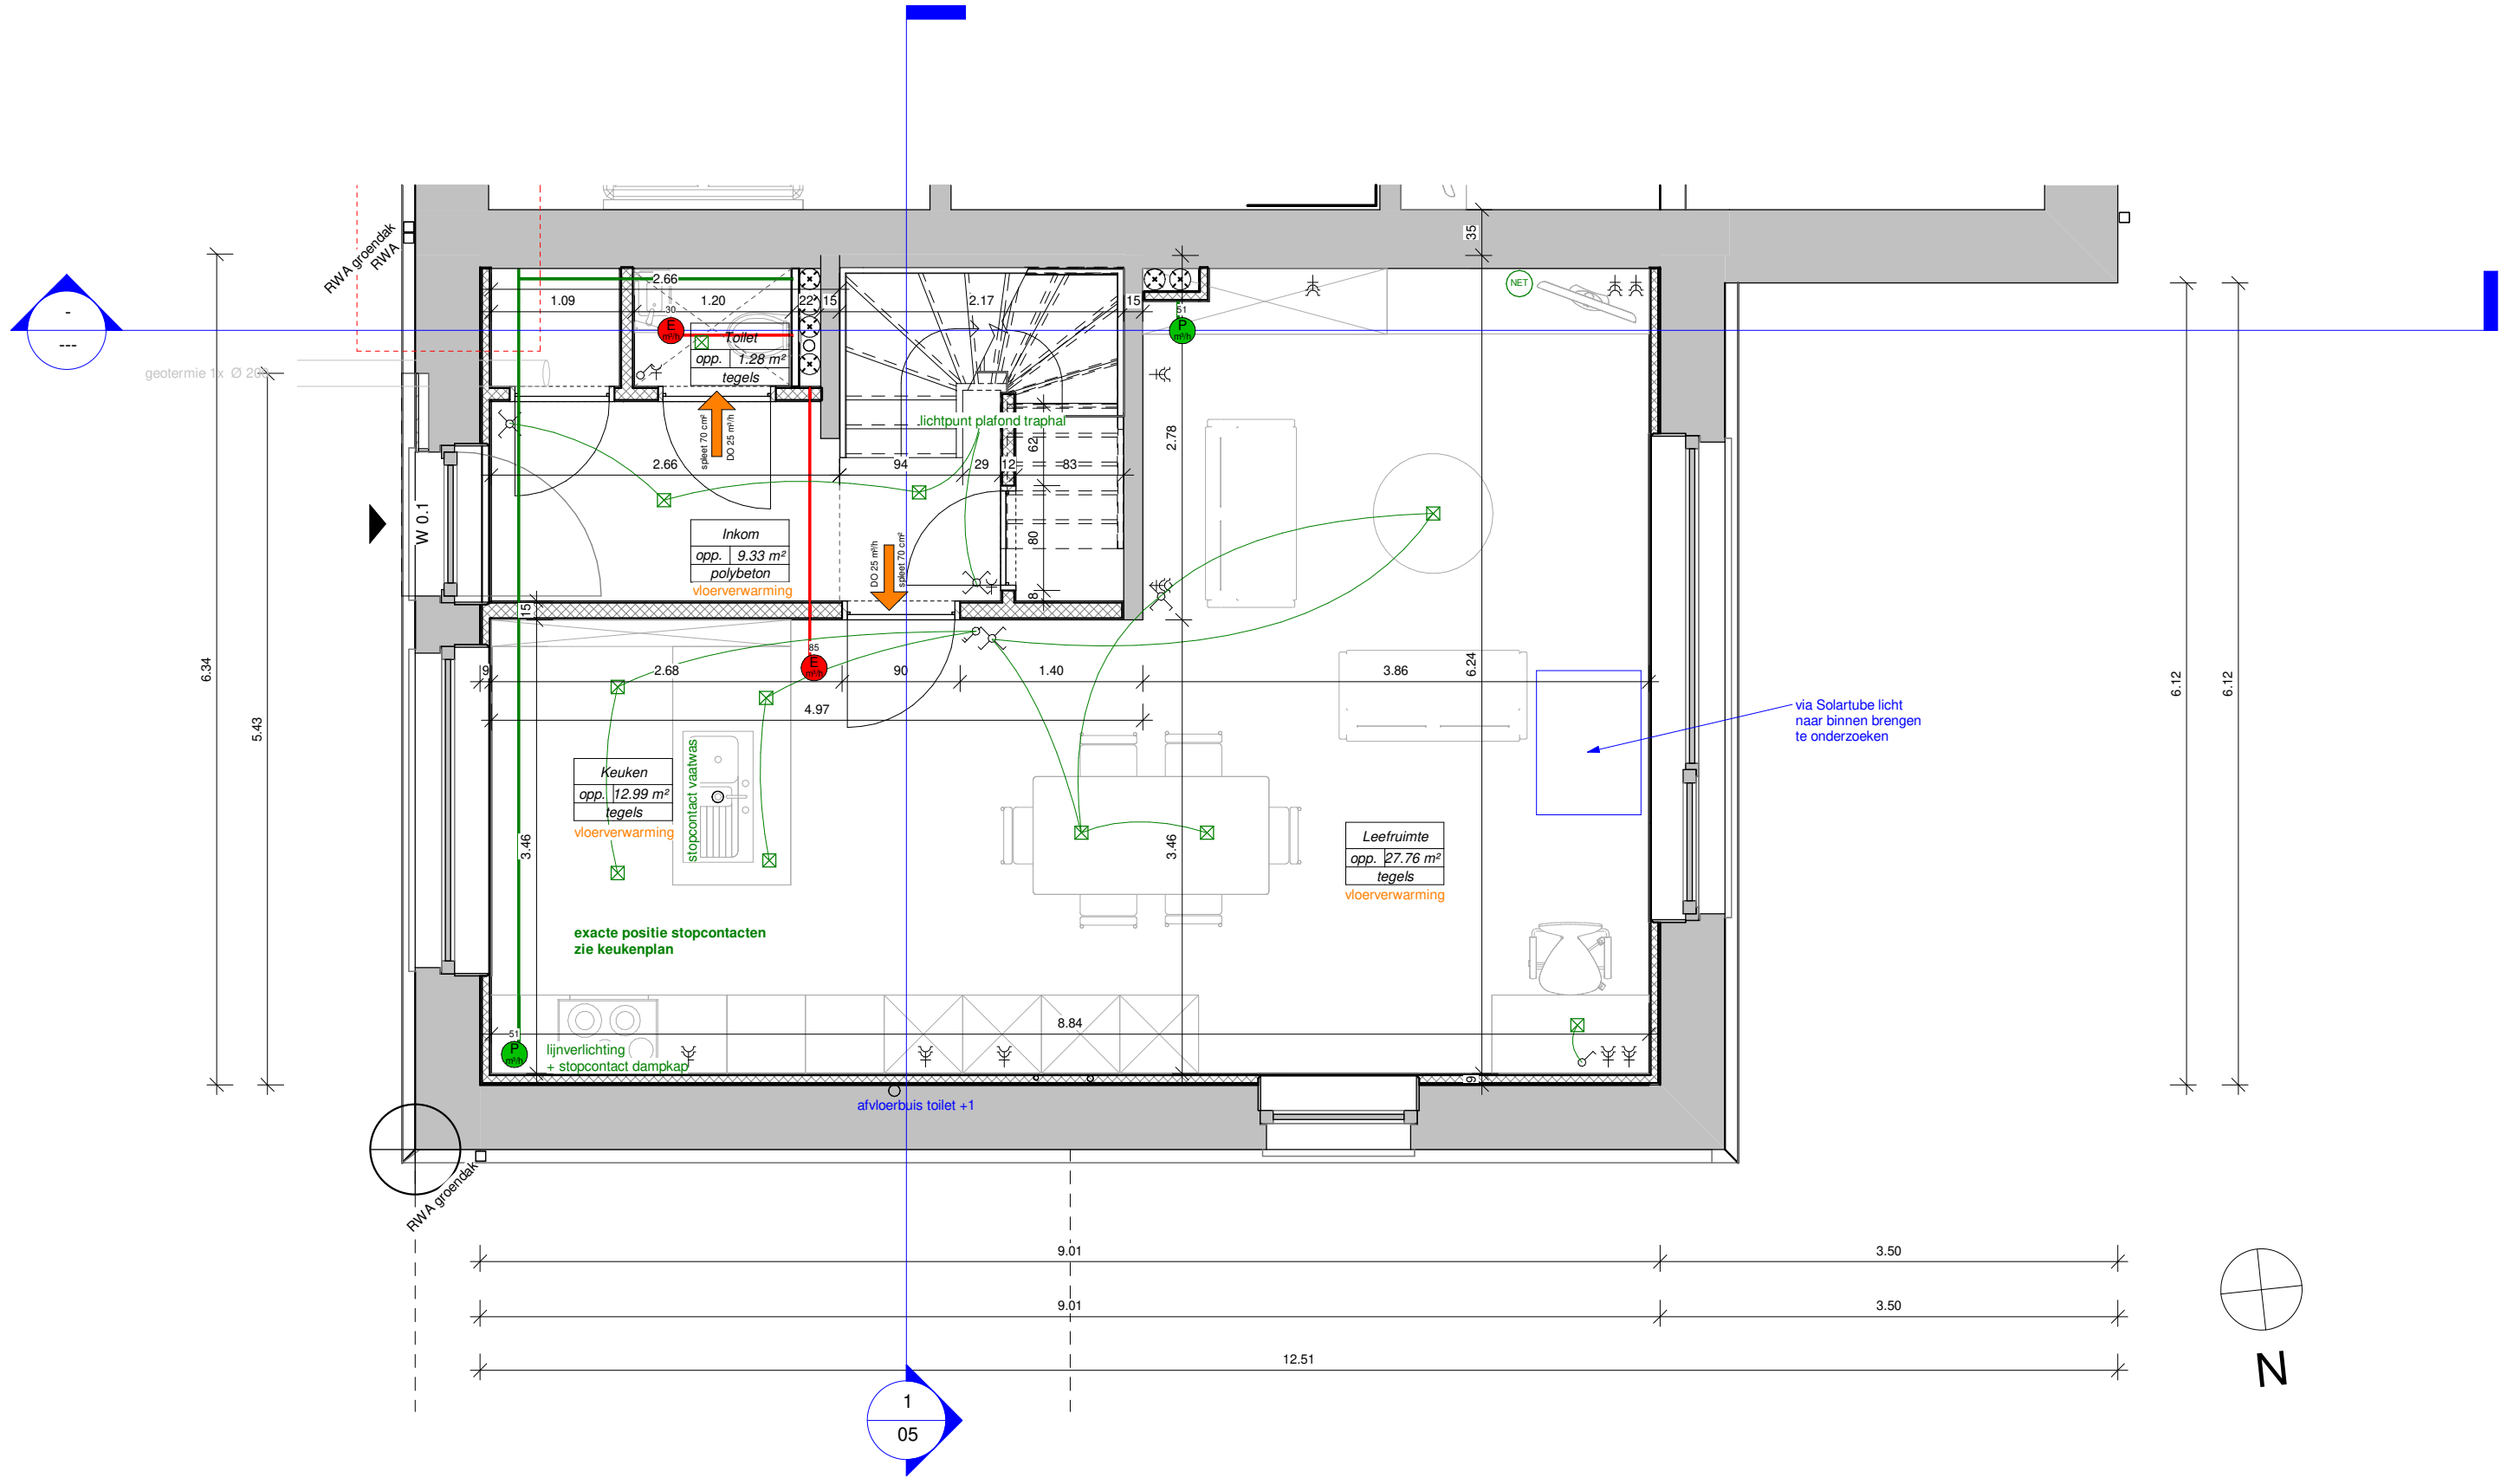

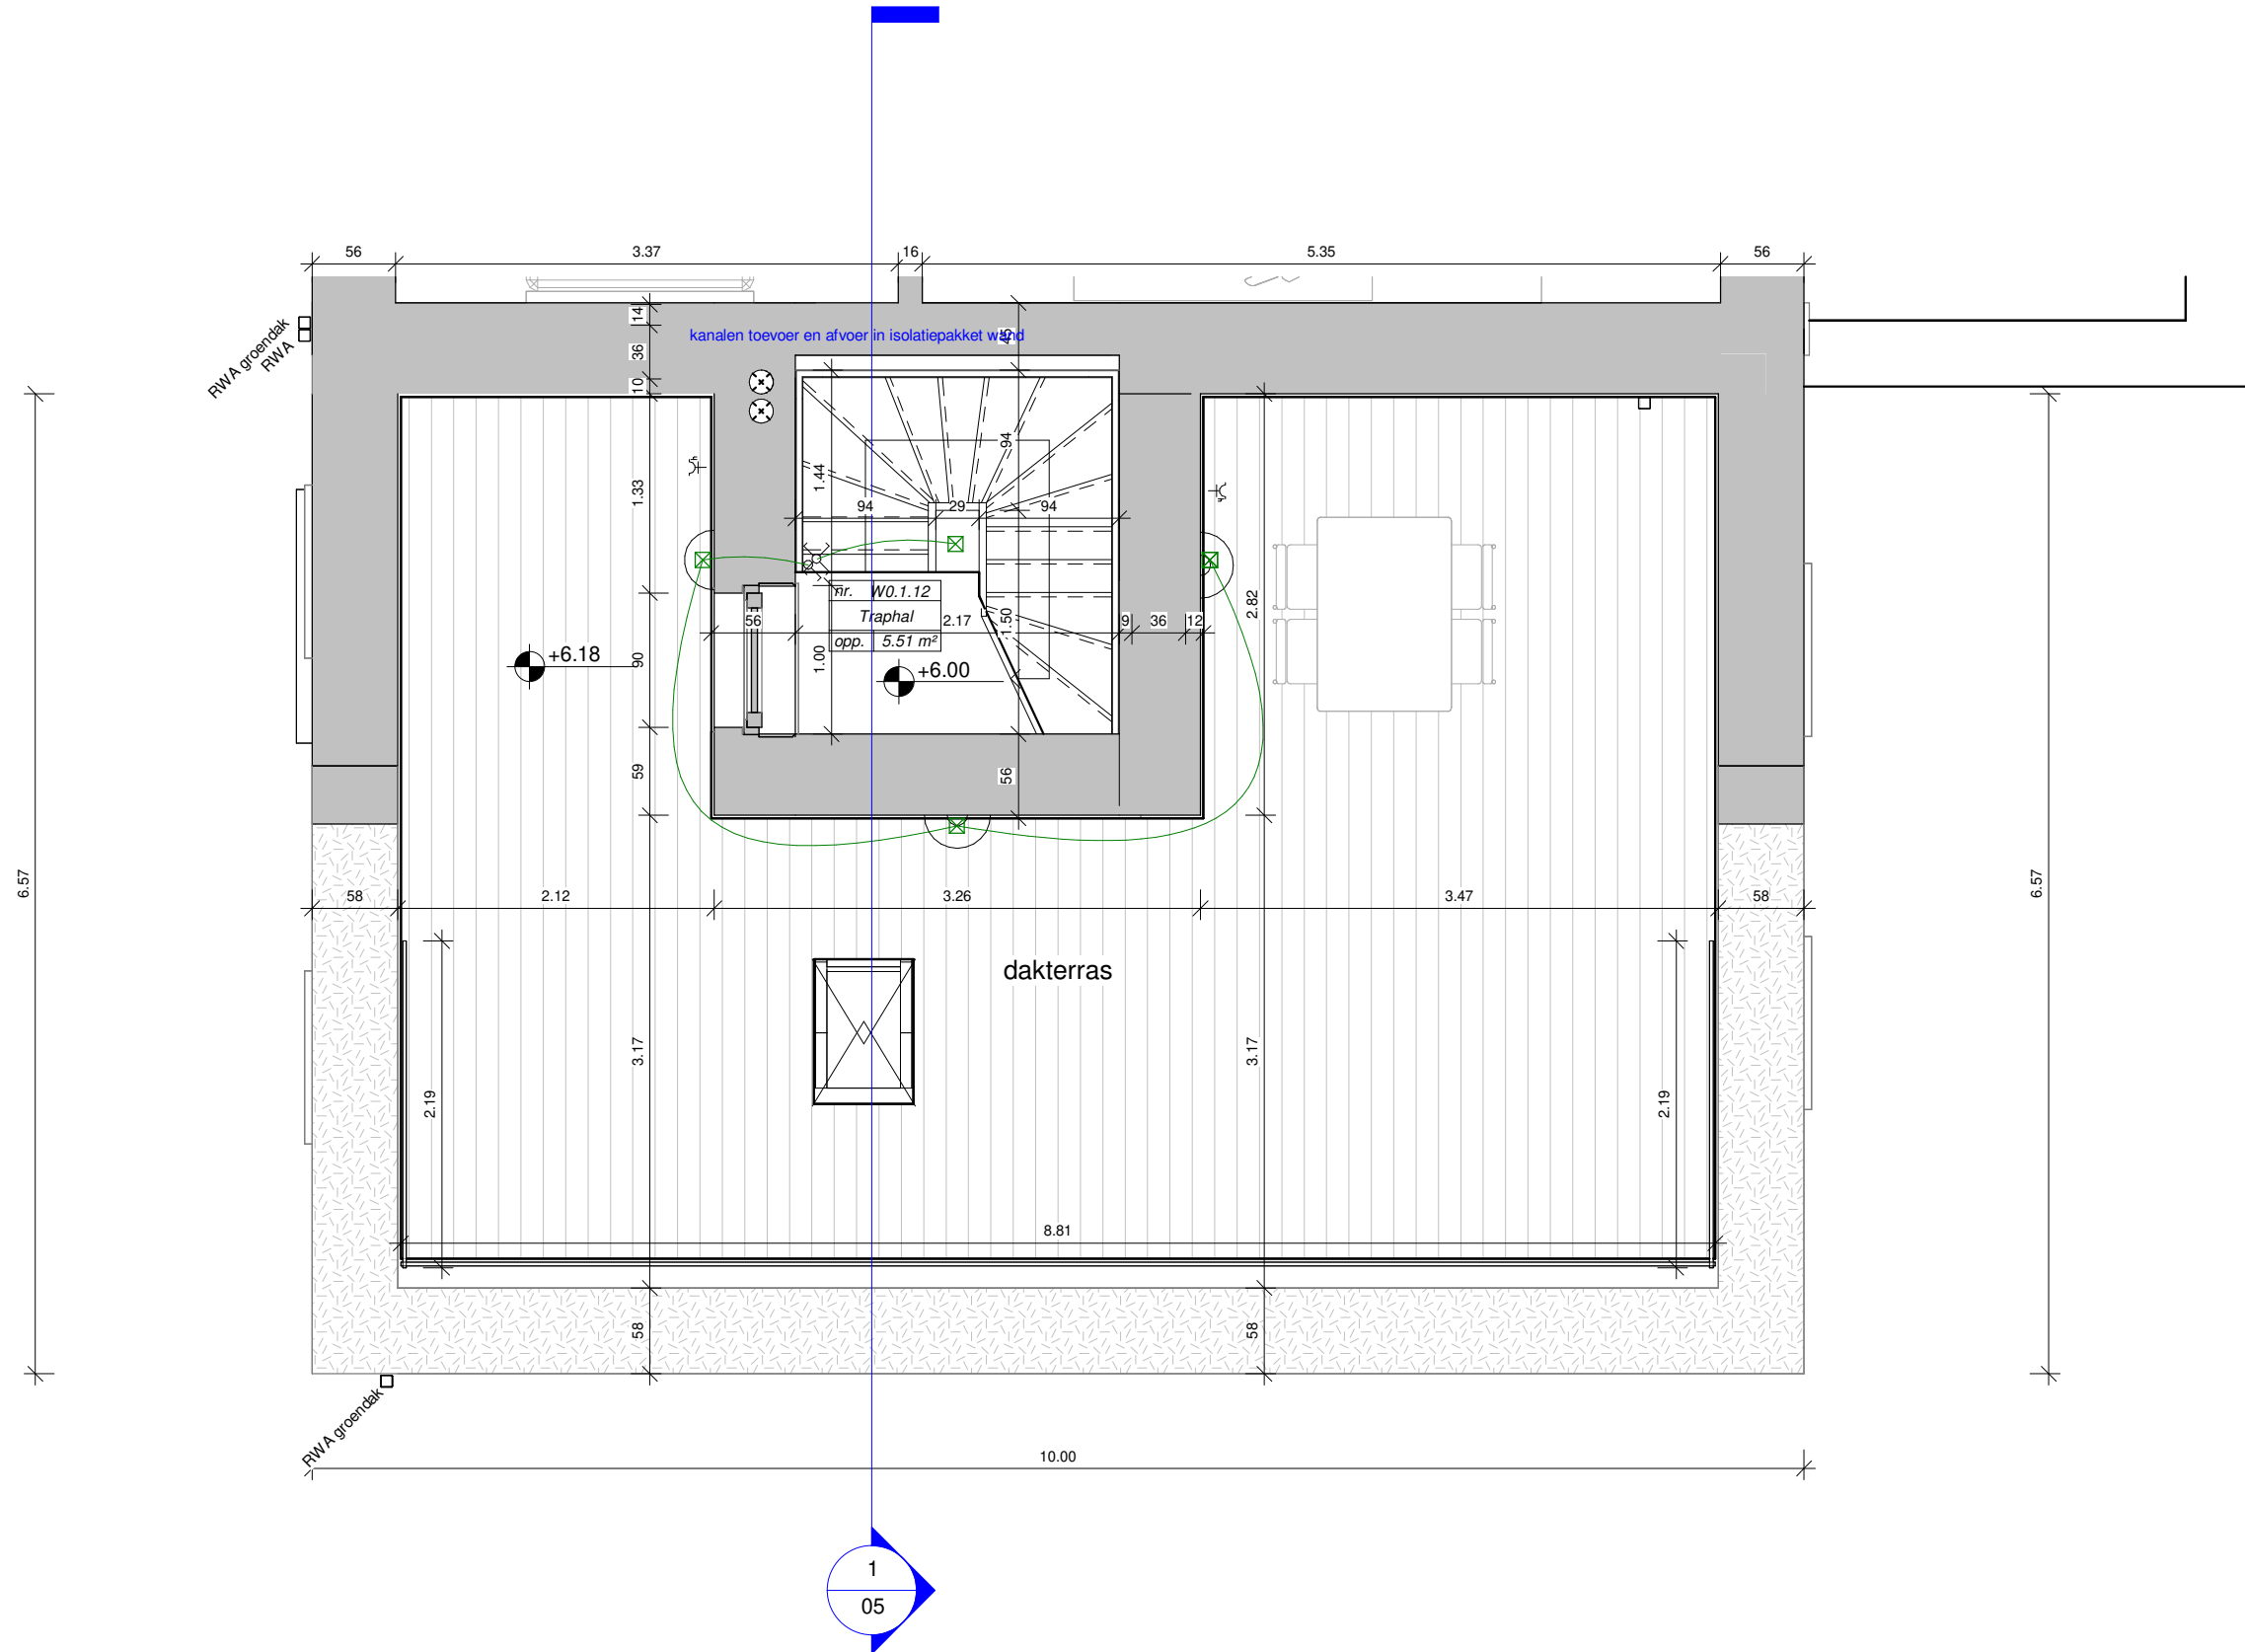

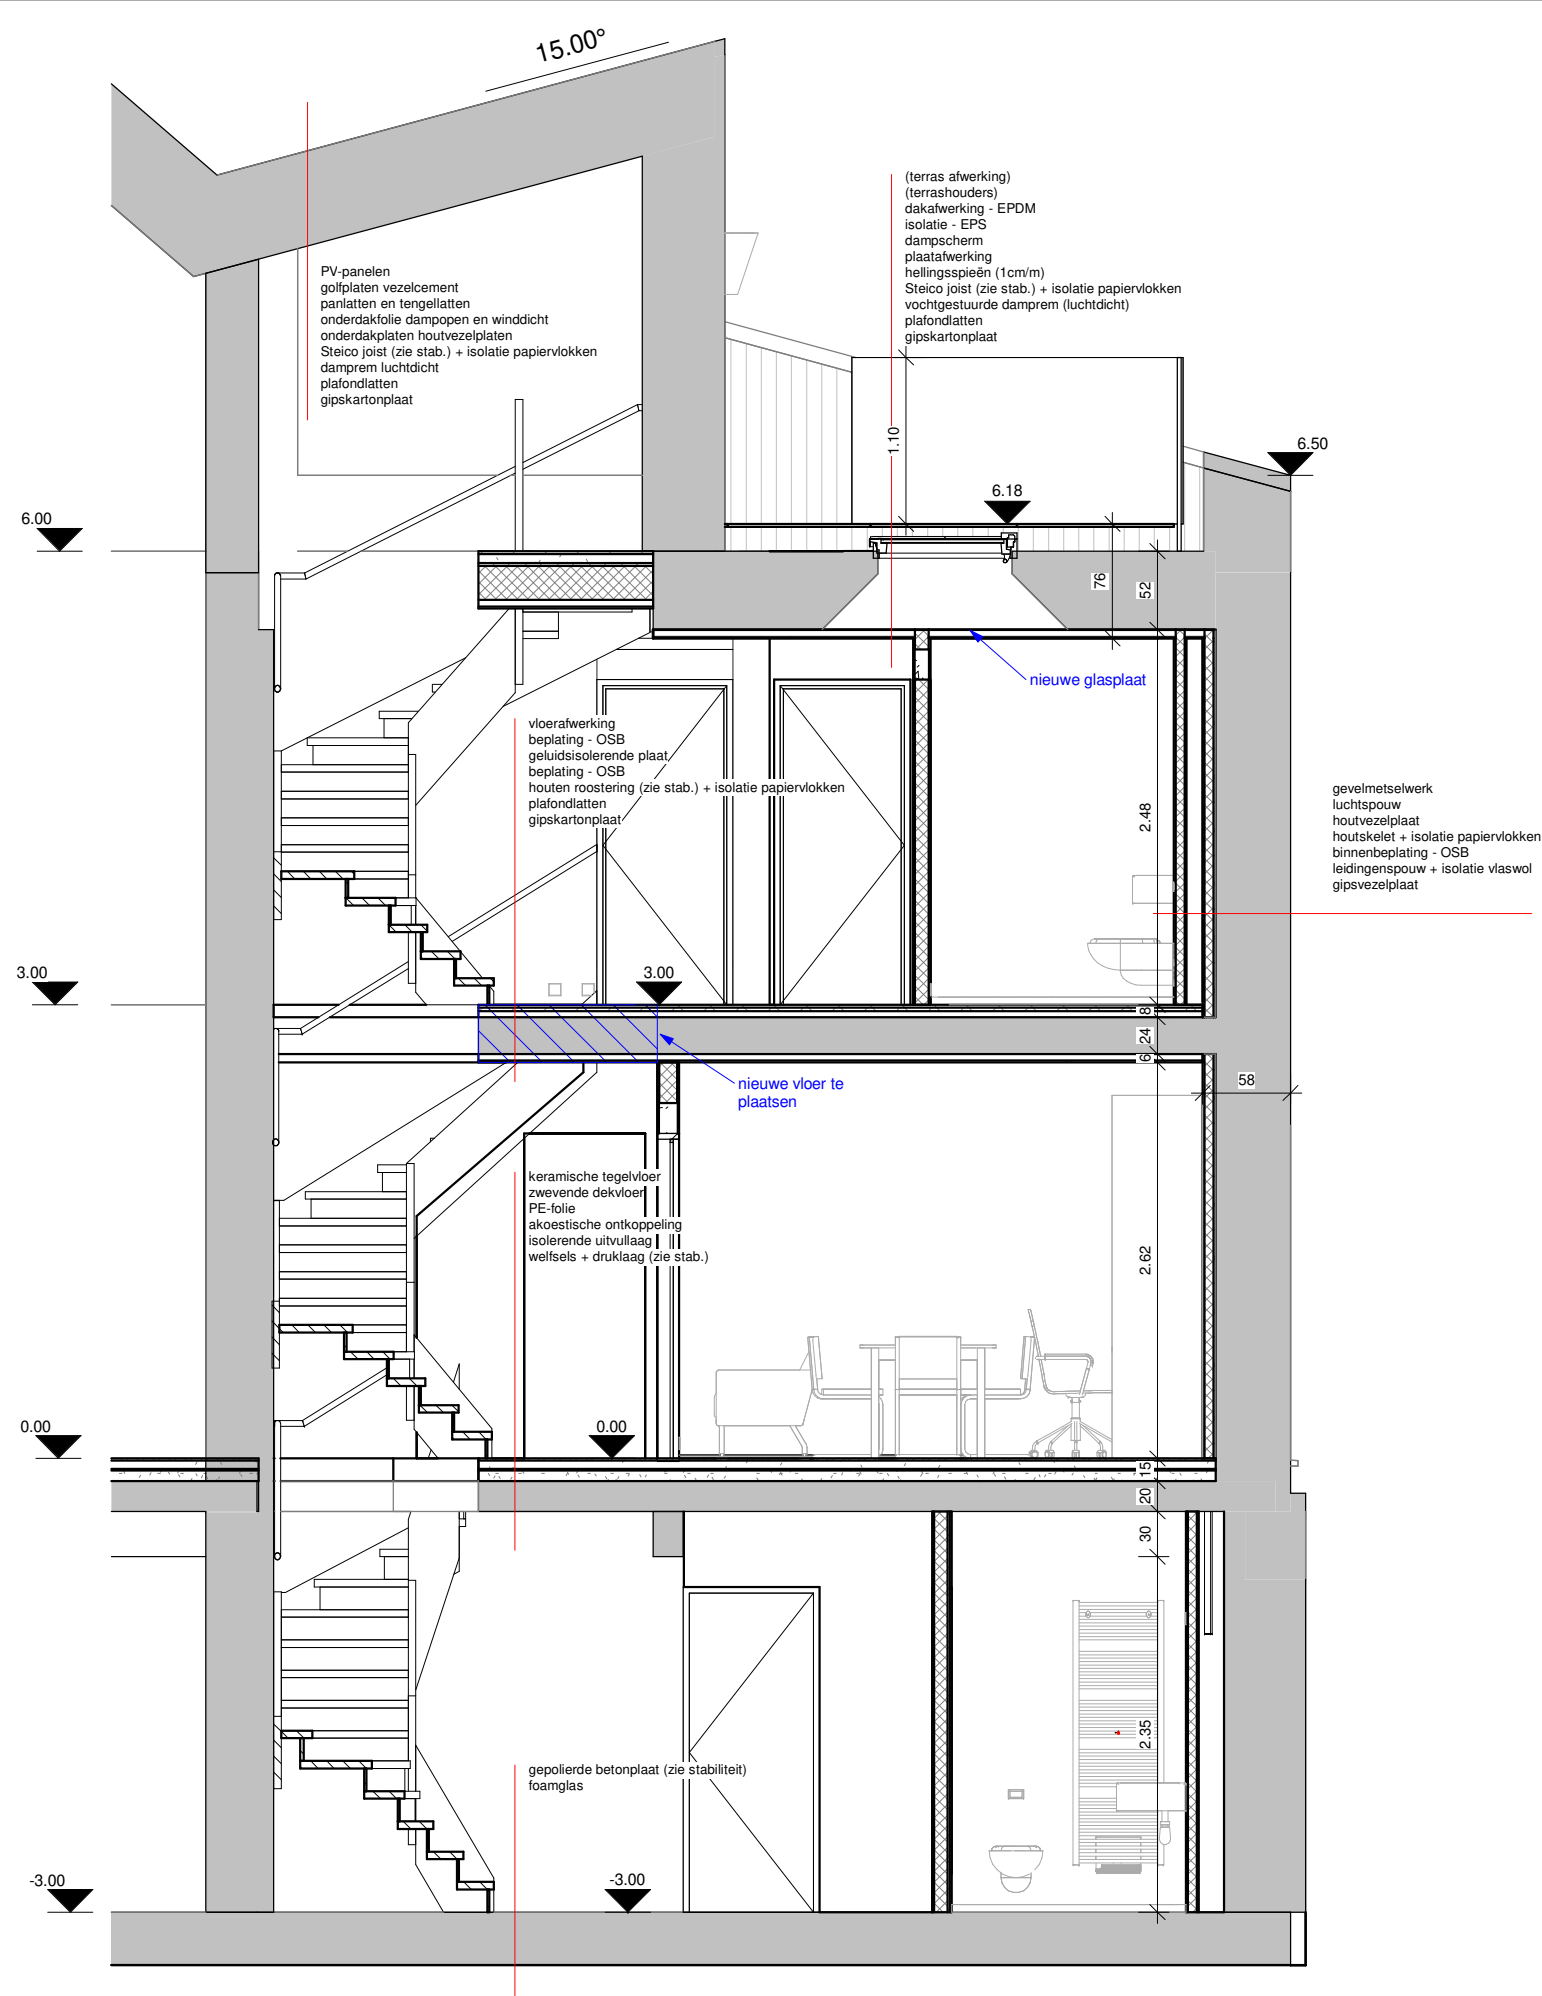

1

1 : 50

Korte snede

ecologische architectuur

eA+

energie-advies

ARCHITECT

EA+ architecten en ingenieurs cvba

contact@eaplus.eu
www.eaplus.euMartijn De Coster
Stijn Van den Broecke0473 86 98 44
0496 72 90 90

BOUWHEER

Cohousing Eikenberg

Eikenberg 27
8310 Sint-KruisTel :
Mail :

WERF

Cohousing Eikenberg

Eikenberg 27
8310 Sint-Kruis
Afd. 19; Sec. D; Nr(s) 113h2+g2+n2+m2+f2

TEKENING

WEST 01 / SNEDE

Plan nr. : 05
Datum : 09/02/2023